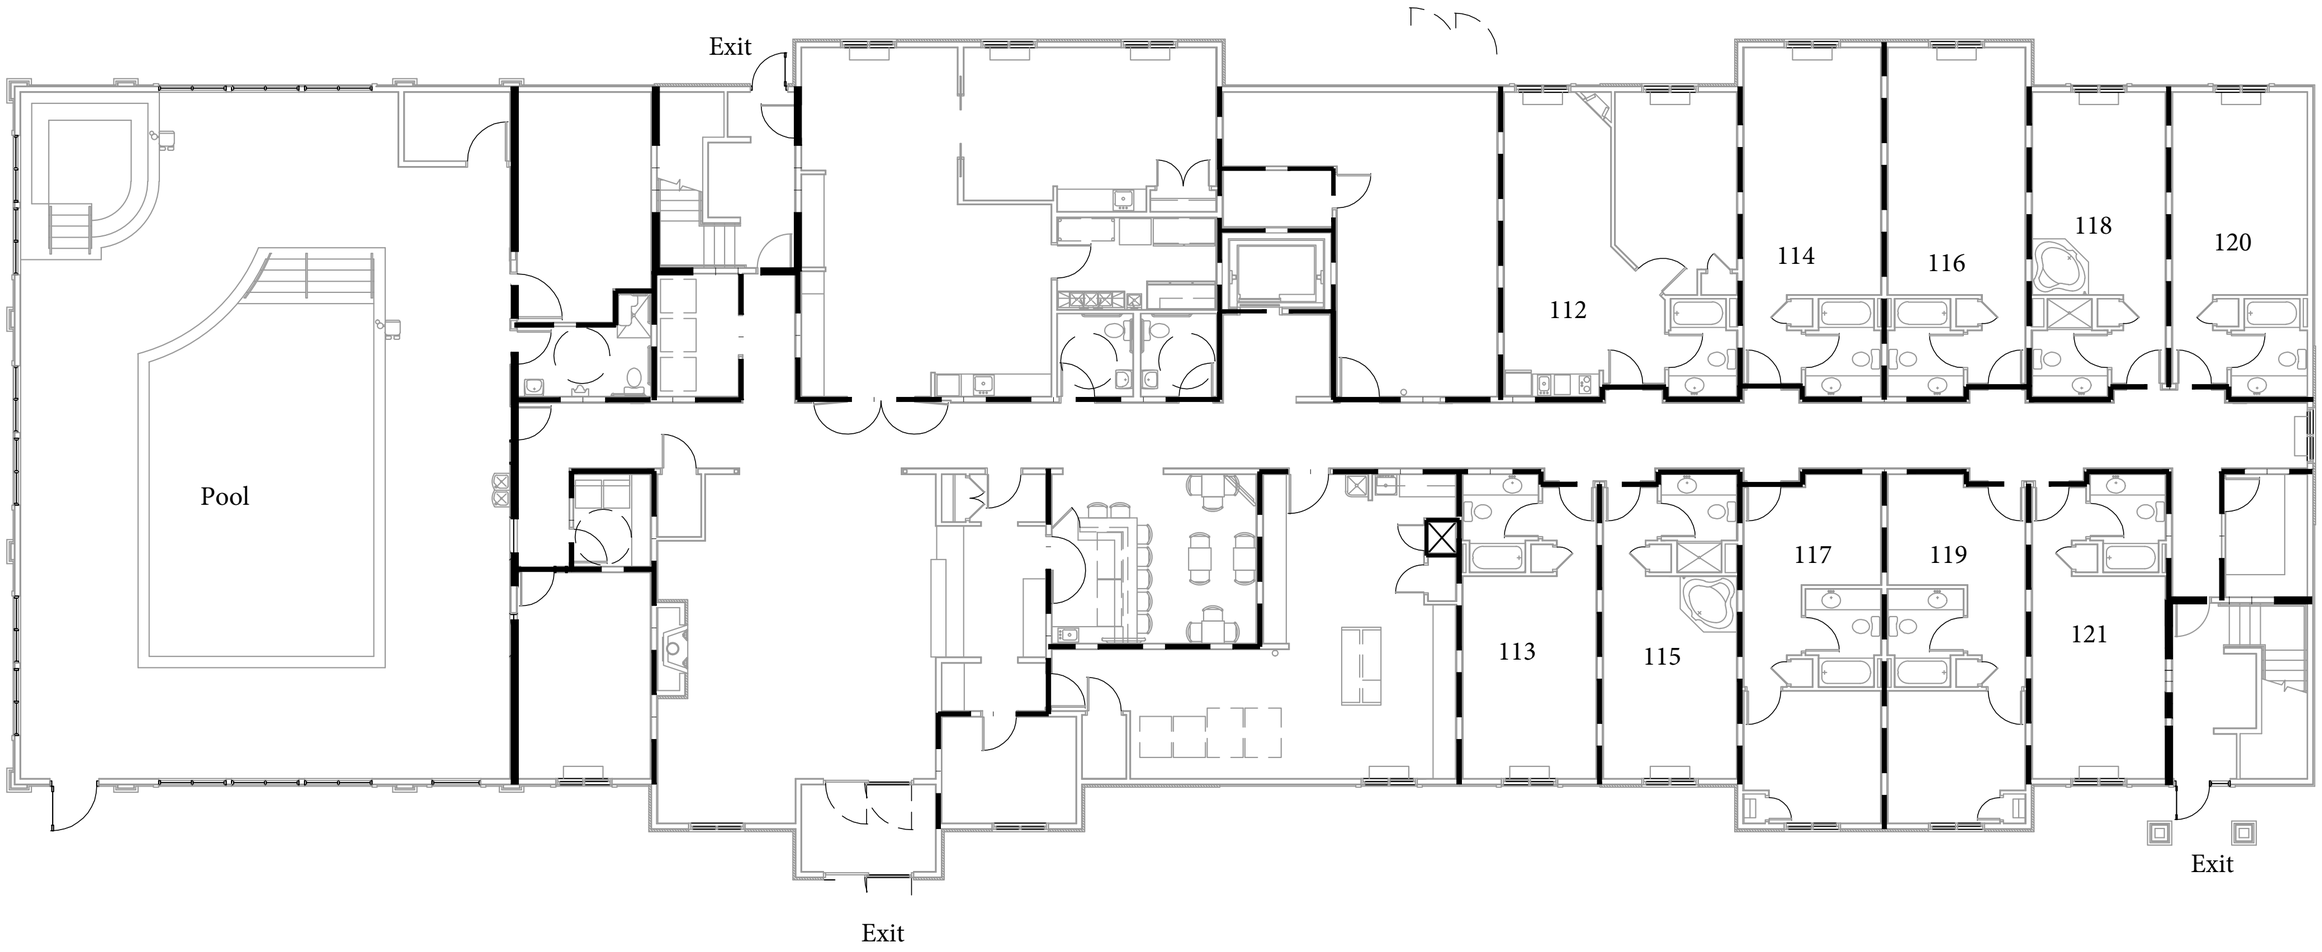

1
T2

FIRST FLOOR FIRE RATINGS

NO SCALE

2
T2

SECOND FLOOR FIRE RATINGS

NO SCALE

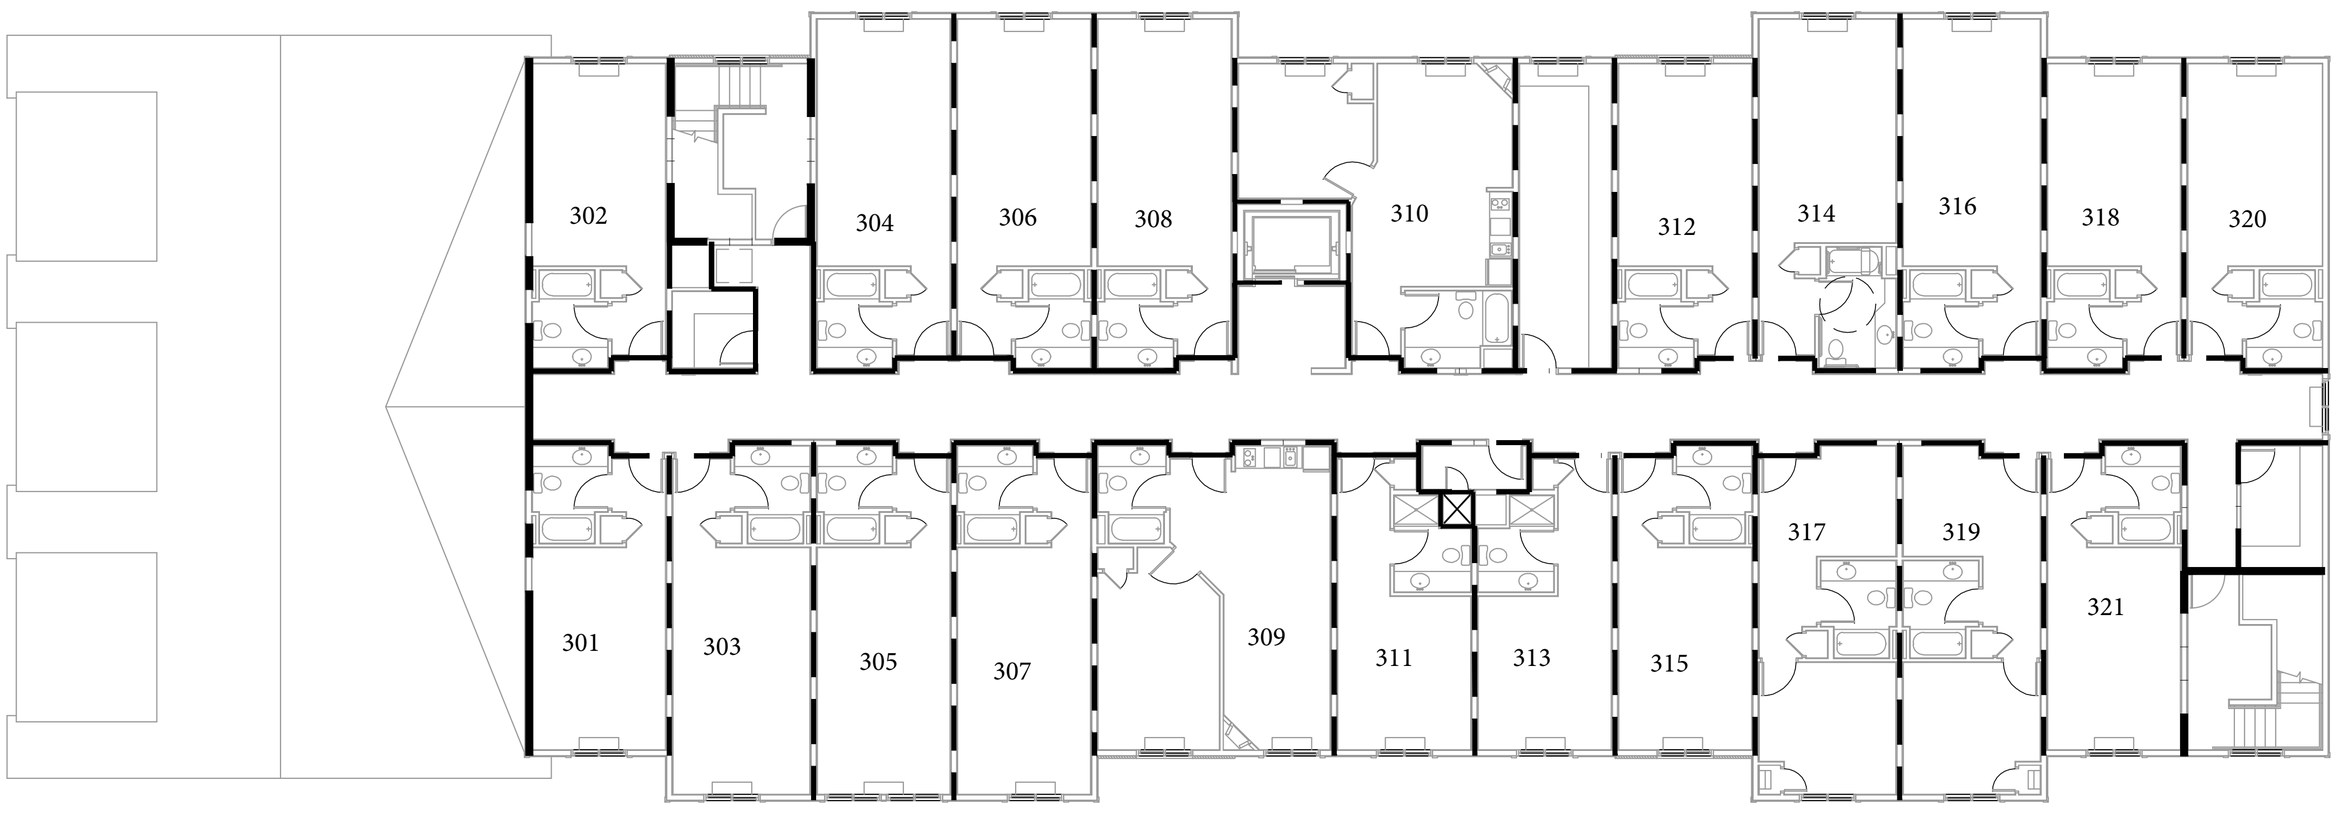

3
T2

THIRD FLOOR FIRE RATINGS

NO SCALE